

Portfolio

André Gonçalves Andrade

More work at
https://aga100kr.github.io/portfolio_aga/


Contents

Drawing	One more tower for a castle	3-4
	Rehabilitation of a Greek town	5-6
Maquette/ handcraft	Housing with alternative materials	7-8
	Earth bench constructed in Crete	9-10
	Lodging inside a cemetery for Art	11-12
	About me	13




Cultural gathering places
Trancoso, Portugal


As an initial response to a town we were still getting to know, we proposed another tower for Trancoso's castle.

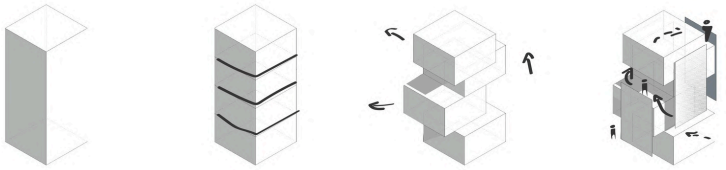


The tower was intended as an isolated viewing experience of the surrounding landscape, hence the slices and semi-solid planes partially blocking the view outside the tower while going up.
The tower was also intended to utilize local dirt from excavations of a project our group would do in Trancoso the next semester.
My role here included AutoCAD drawing, some sketching, and building a 3D model that served as the basis for developing the project and presenting detailed sections.

Group: Me, Débora Barros, Roberto Pereira

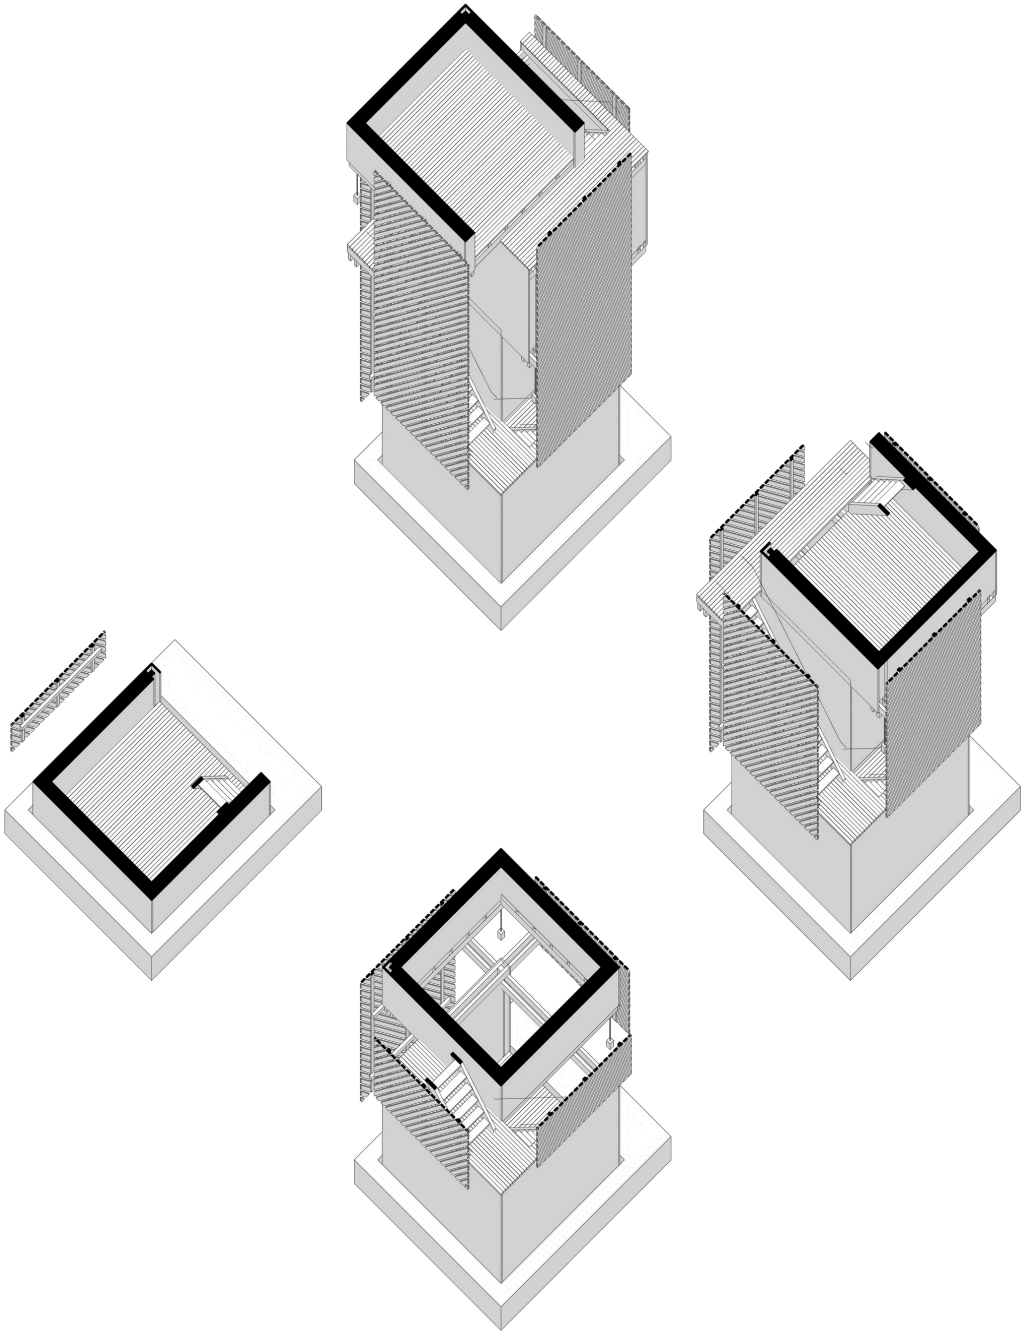

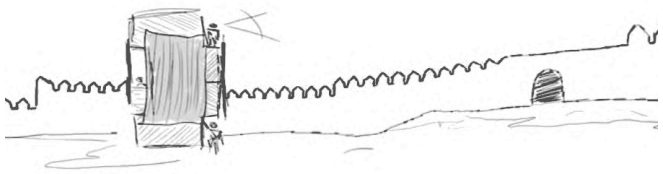


855
Planta de
Piso 1
(+871,5m)
N
1:200

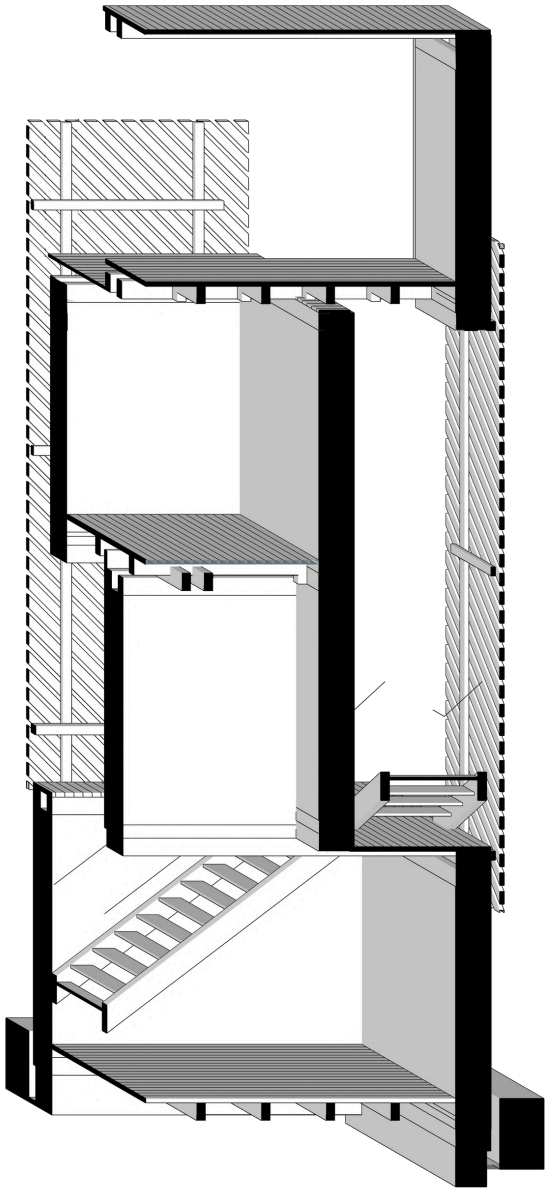






Landscape reconfiguration
Chaniá, Greece


The beach town of Stavros in Chania has the problem of being abandoned during off tourism seasons, and my group had to solve this issue. We intended to introduce objects into the landscape as landmarks (my colleagues' job), while allowing for enjoyable walks between them (my job).

Group: Me, David Romero, Joel Gras

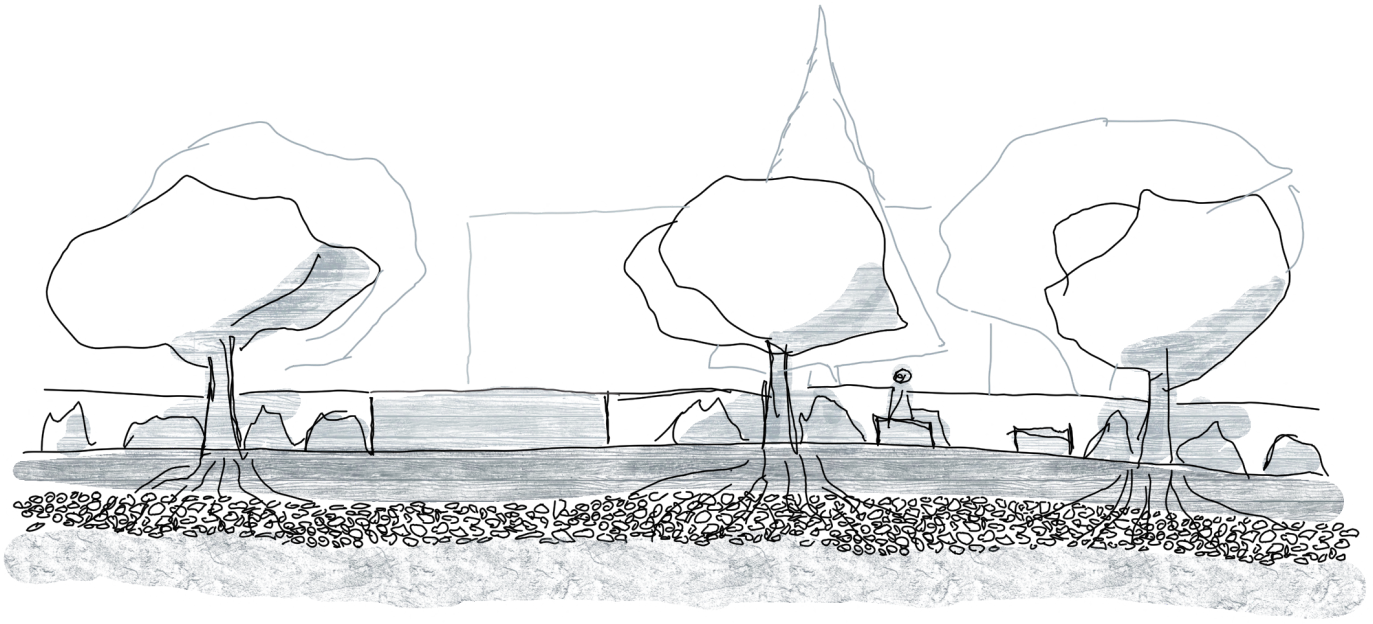


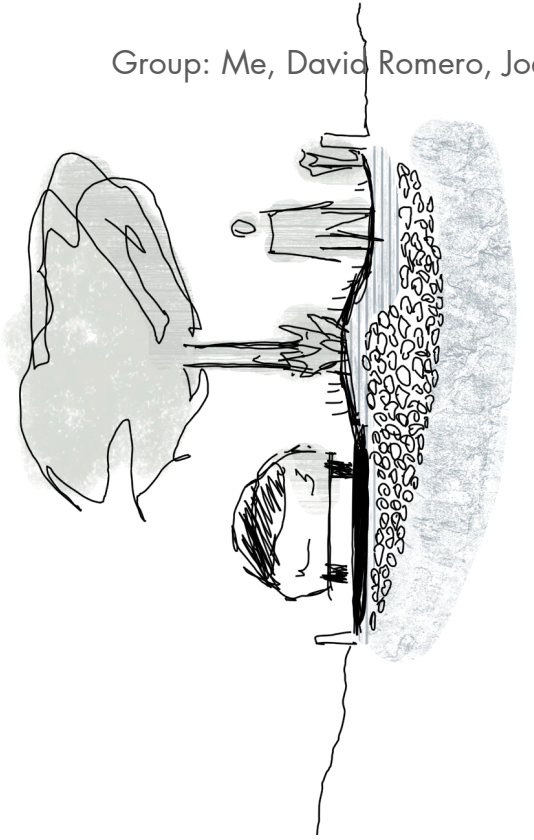

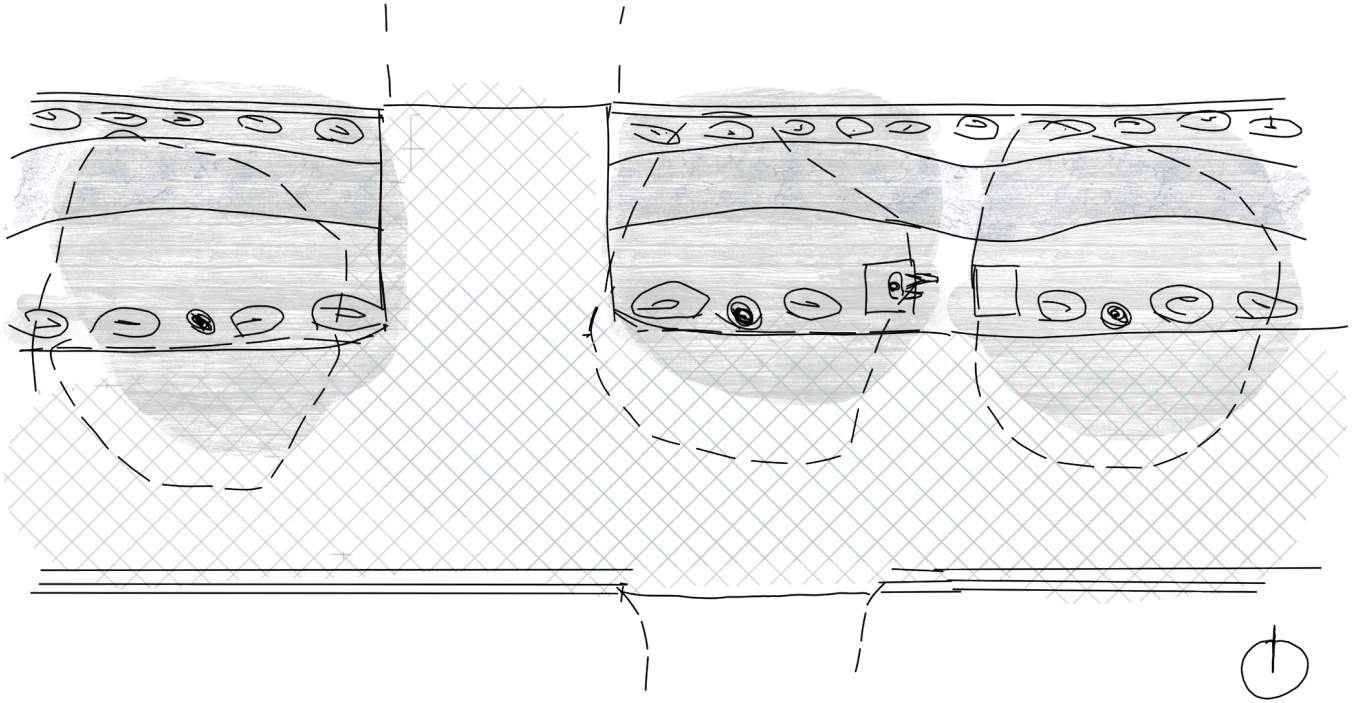

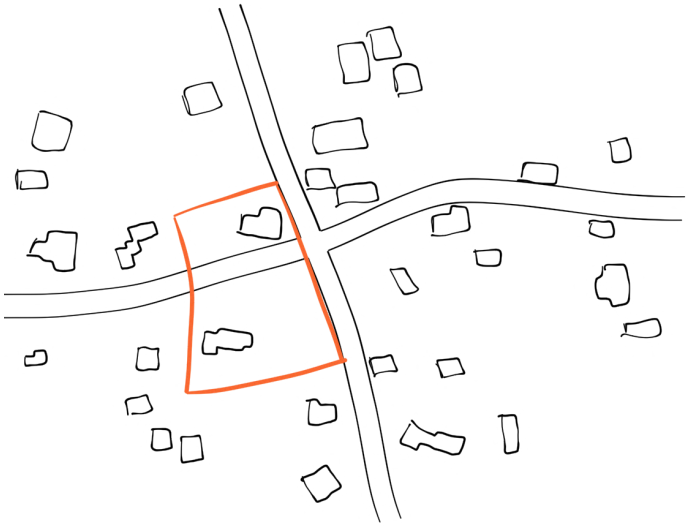

Hence, I reorganised the street network to improve pedestrian movement, including along existing unpaved roads. The proposal incorporated local, aromatic plants, whose qualities would be enhanced by the warm climate and constant sea breeze.

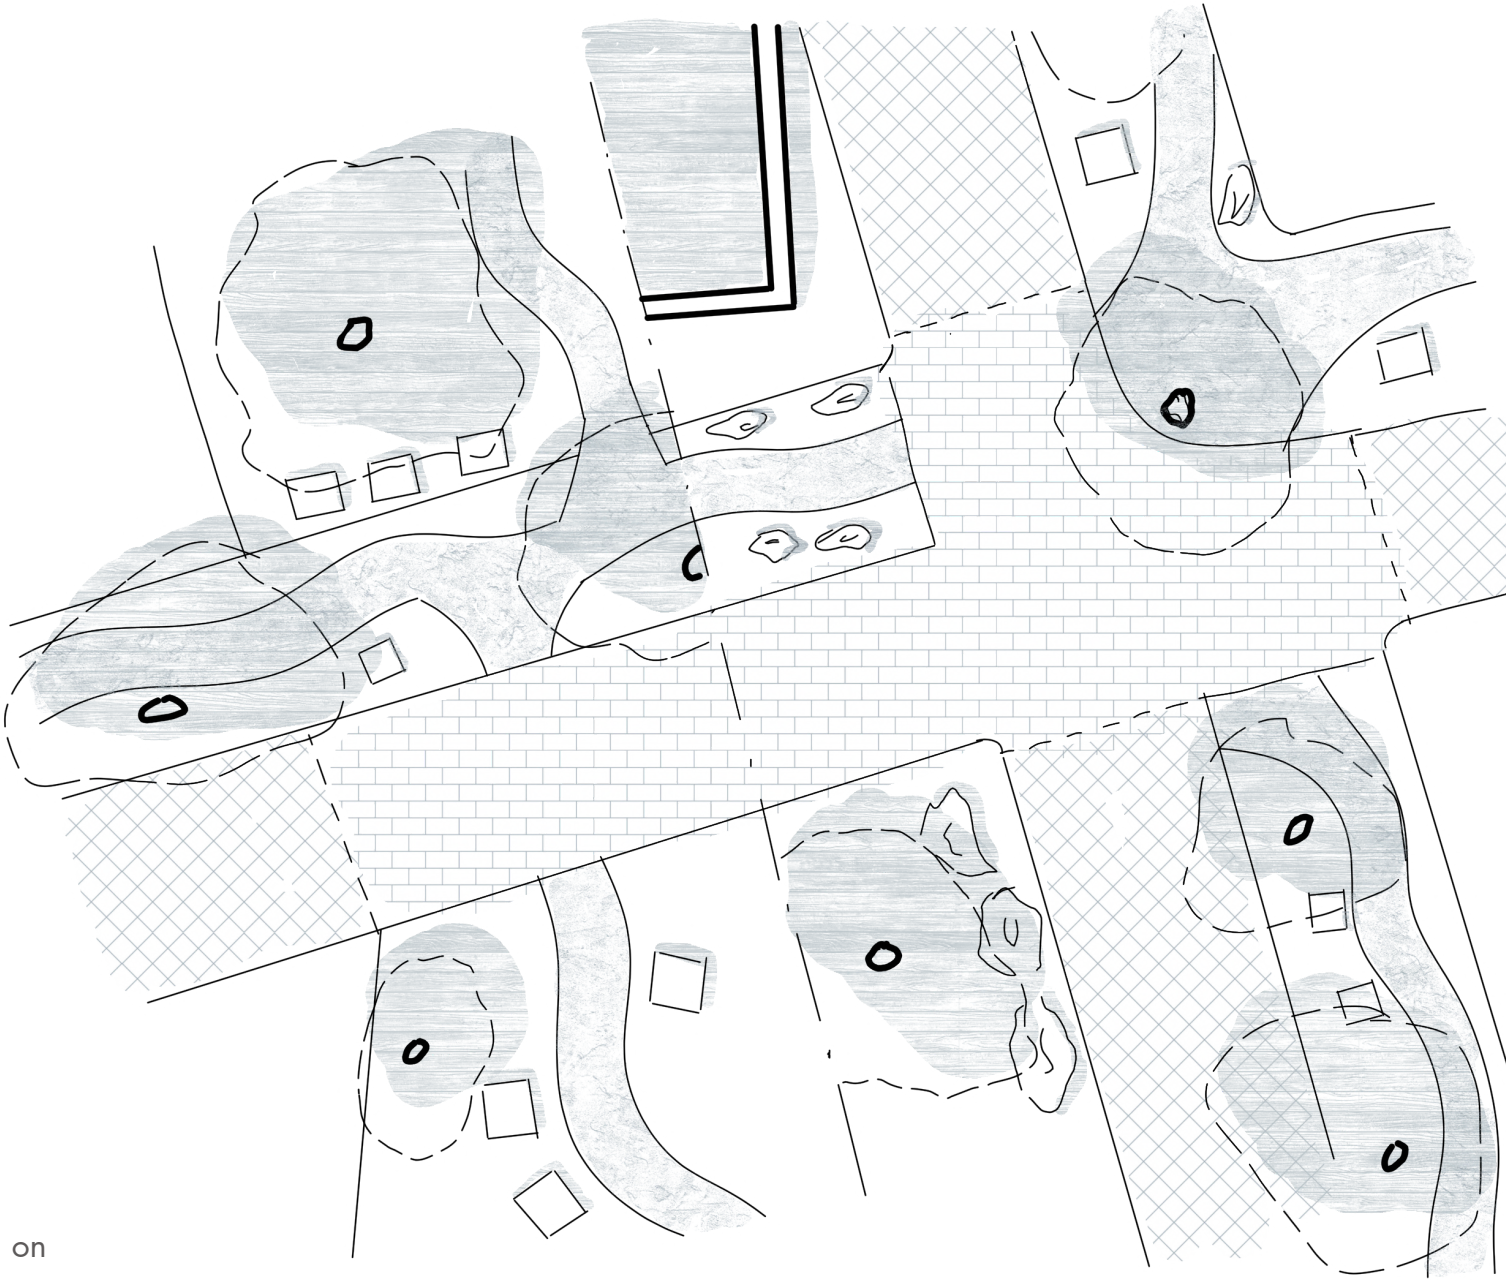

Vehicle and pedestrian path

Vehicle pathway


Example of connection on Stavros' central cross

https://aga100kr.github.io/portfolio_aga/media/stavros



Social Housing & Co-living
Fundão, Portugal

Propousal for Social Housing and Lodging for the town of Fundão, Portugal.
Seeking to maximize the amount of public space available, both buildings are elevated above ground level. The lodging complex (the smaller of the two) was intentionally shaped to provide shade during the scalding summer days, as temperatures in Fundão often exceed 40°C on multiple days each year, while winters can reach 0°C or below. Due to this location's thermal variation, I thought that a good thermal mass and insulating material would be a good addition to the buildings, so I proposed using papercrete, developing some mockup experiments at 1:1 scale - pavement, wall section and simple block, from left to right, clockwise.

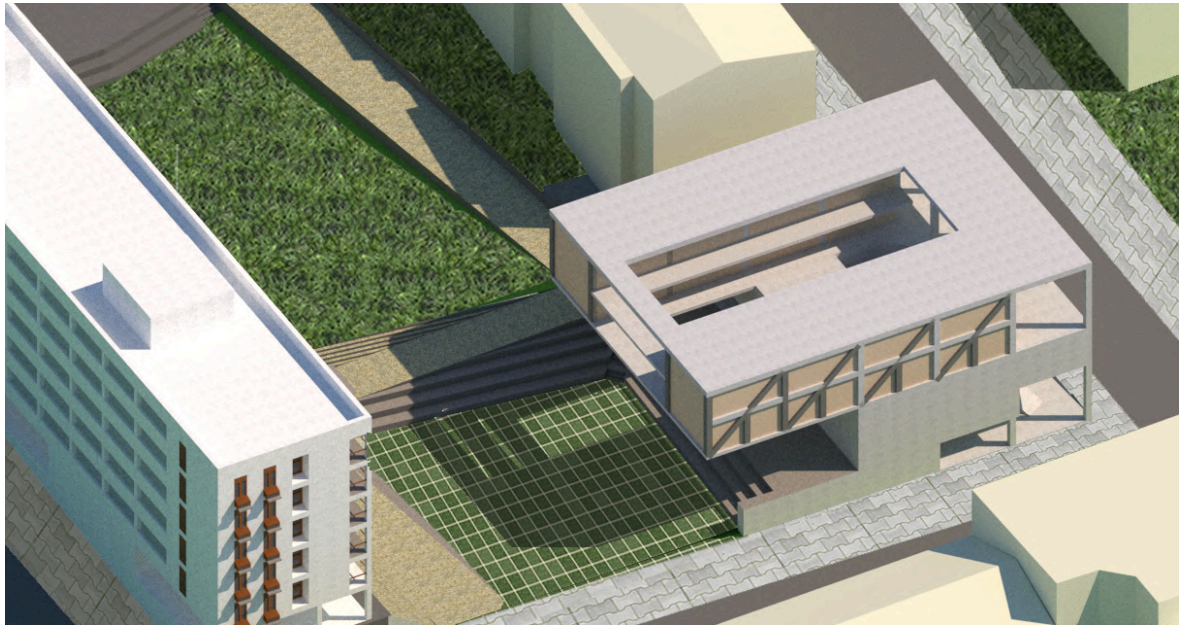










Lower and upper plans of the Co-living complex

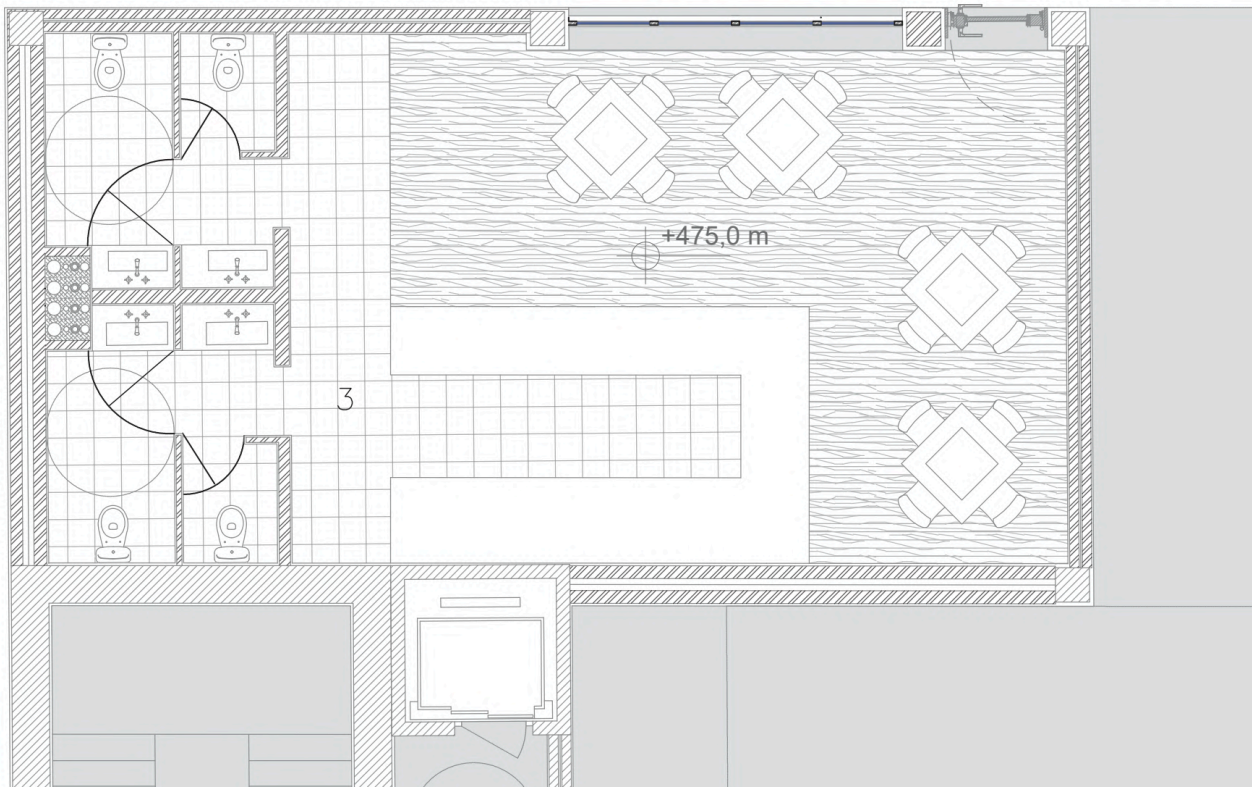

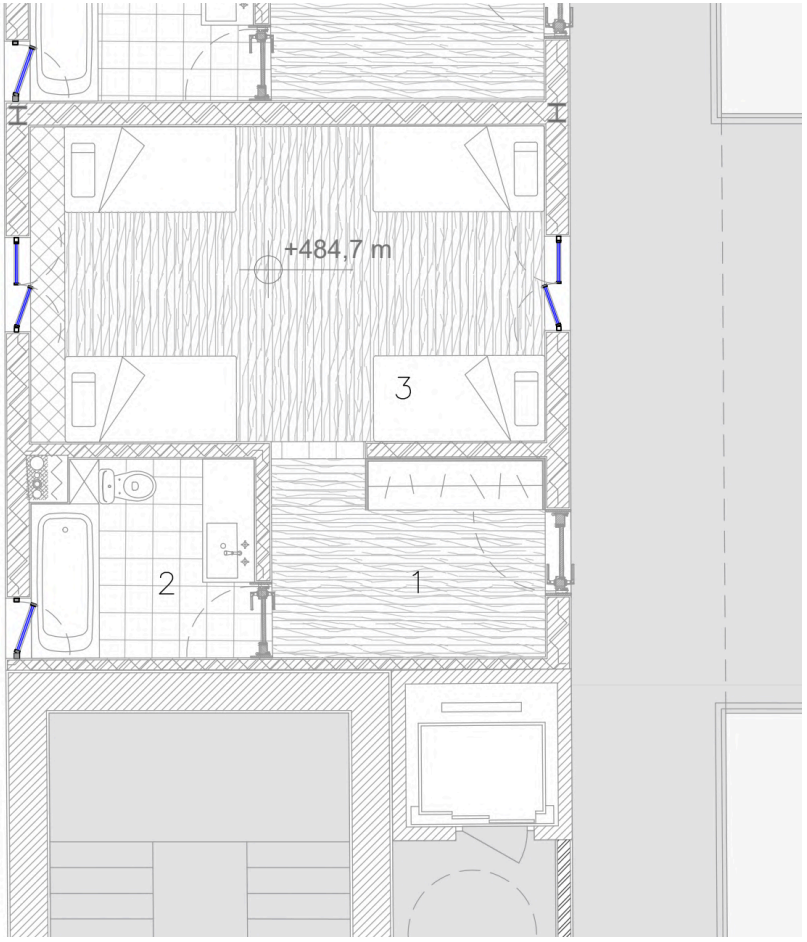

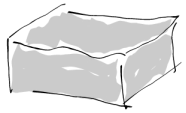

Sitting bench
Chaniá, Greece

During my Erasmus in Crete, Greece, I got an assignment on construction with natural materials (Ειδικές κατασκευές με φυσικά υλικά). The intent of the assignment was to let students understand how the material works, by planning and building a 1:1 scale model with our hands. Our group decided to do a small, yet quite challenging bench made entirely out of adobe bricks, hugging an olive tree.
My role in this project was mainly to figure out how to keep it from falling apart, its orientation and final 3D scans and modeling/drawings.

Group: André Andrade, Catarina Viegas, Sidar Timurturkan, Yaren Tanriverdi








3d scan of the finished work and photo of the bench


https://aga100kr.github.io/portfolio_aga/media/bench




Artist Lodging/'Shrine'
Morille, Spain


This project aimed to utilize 4 border cabins as artists' lodging for the small village of Morille, where art is buried in a graveyard. This reminded me of tales of ancient Celtiberian rituals, megaliths and their monumentality. I aimed to create a ritual place, on a small scale, with the necessary lodging for 4 seperate artists, utilizing the existing cabins on site, to foster the act of burial (the artist has to feel like they are on the frontier between life and death).

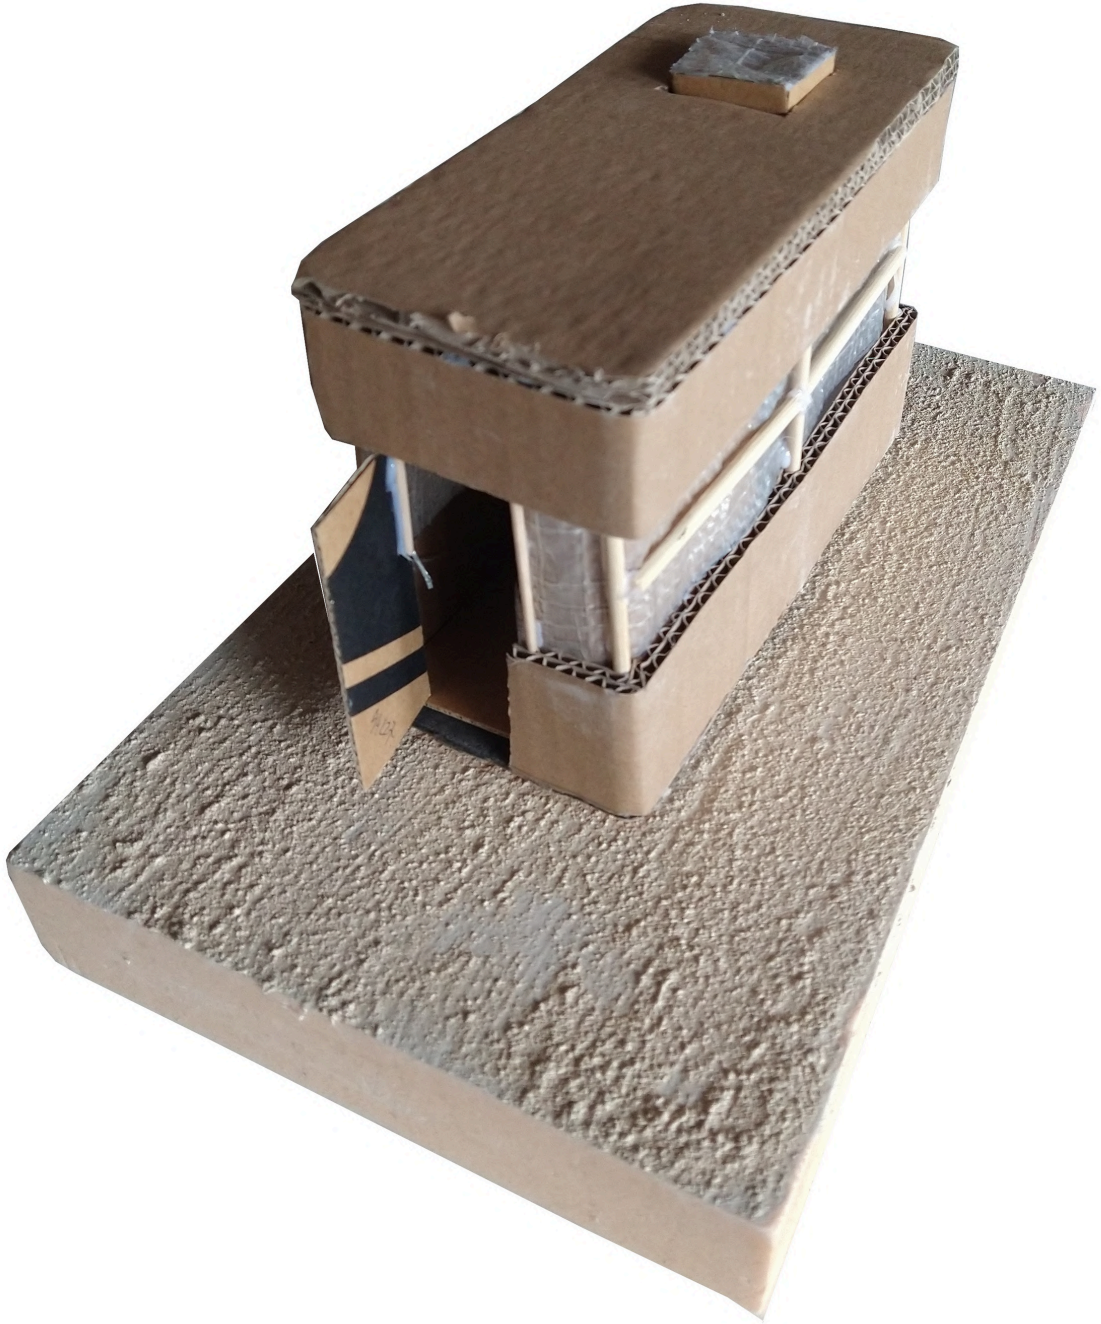

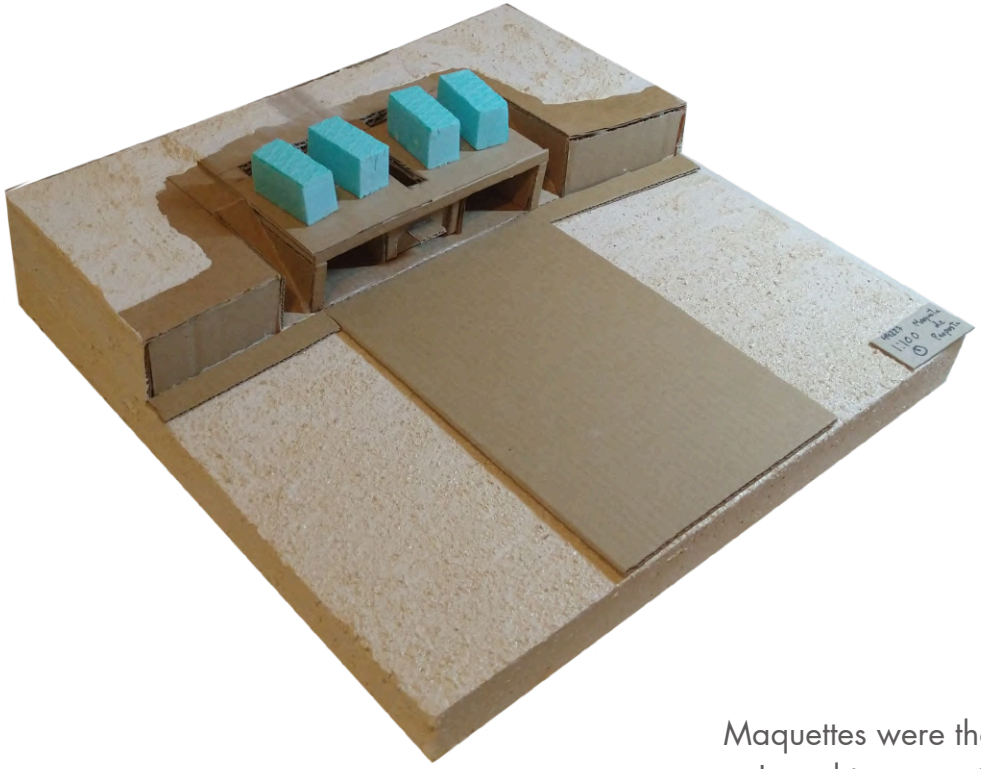

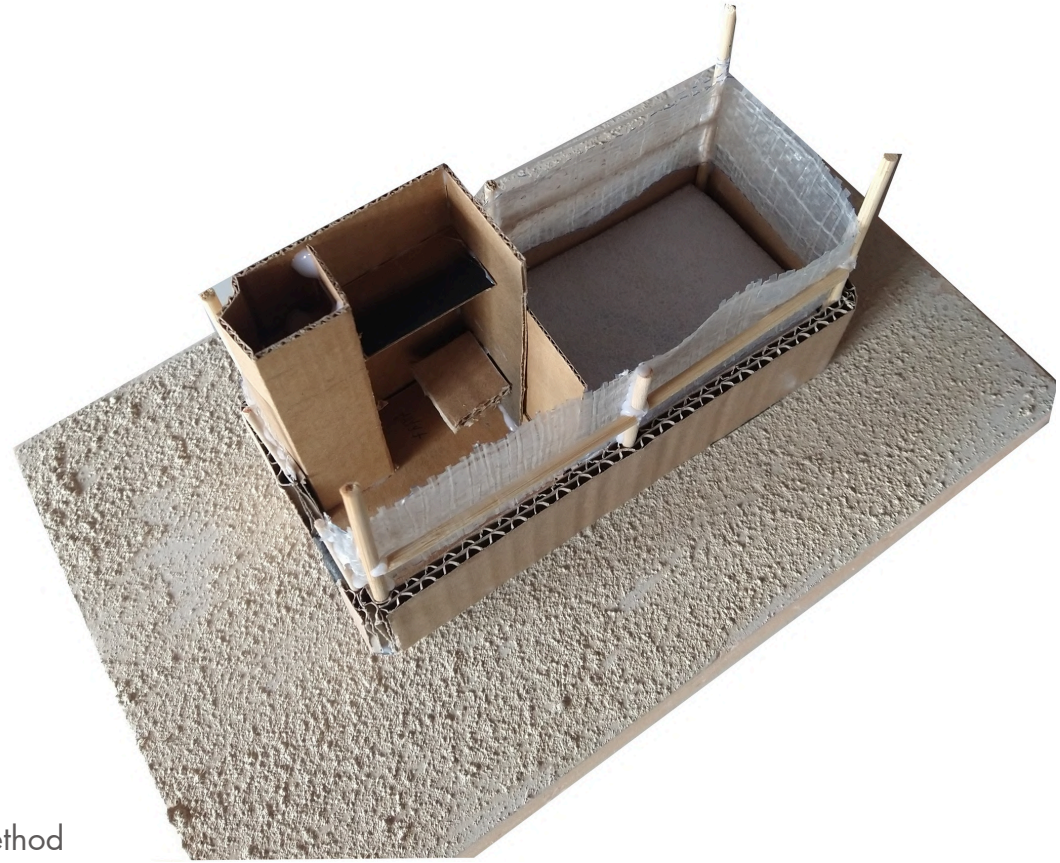

Maquettes were the only method
I used to present the project

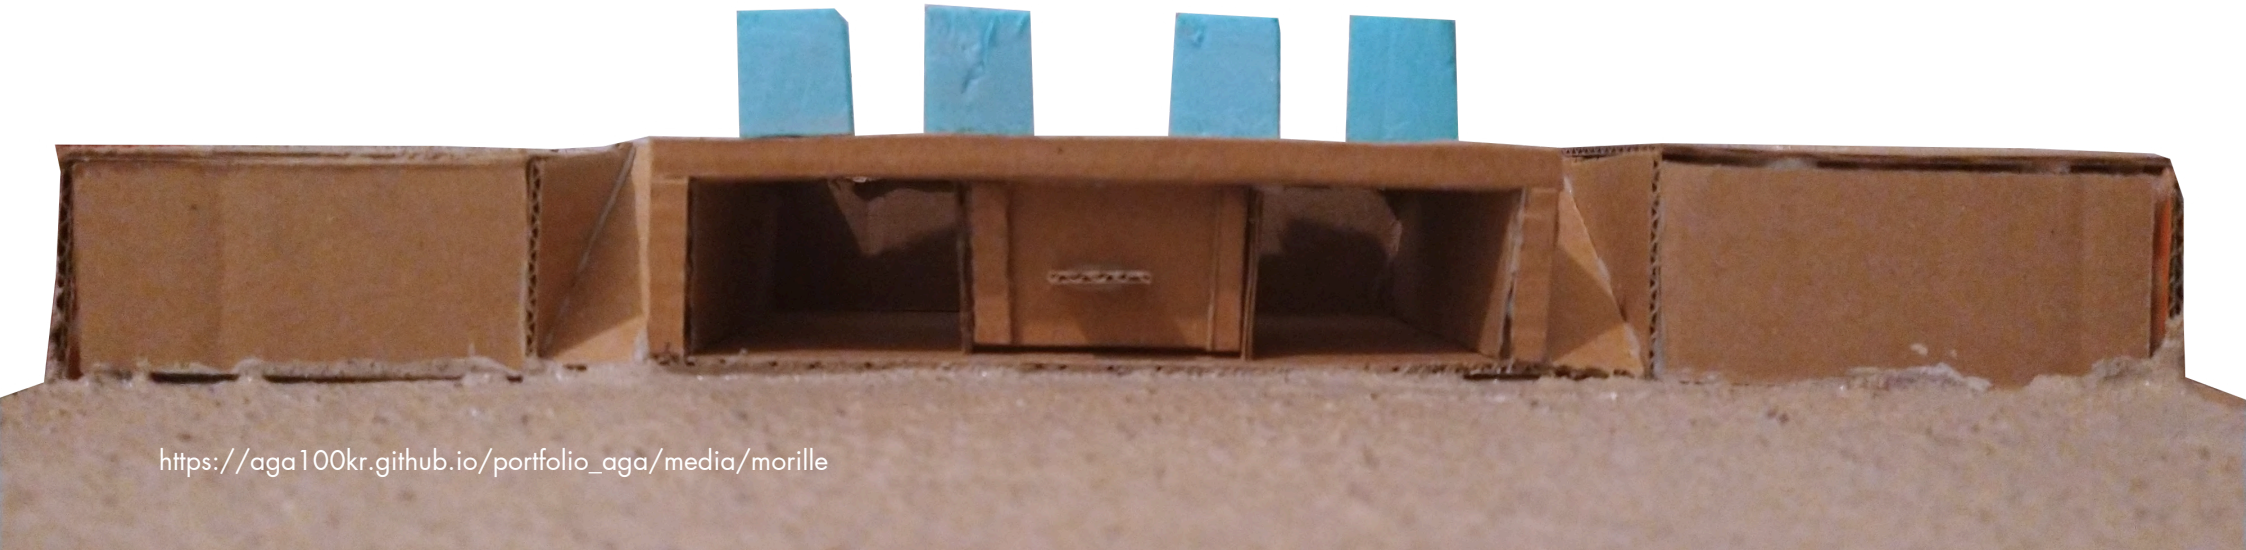

https://aga100kr.github.io/portfolio_aga/media/morille

Education:

Bachelor's and Master's degrees in Architecture at the University of Beira Interior 2019/2026 (finishing Master's Thesis)
Erasmus Exchange: Technical University of Crete 2024/2025

Something about me:

Passionate about alternative model making and interested in Architecture with natural materials. Also interested in Free and Open-Source Software applicable in Architecture. Wishing to learn about maritime architecture.

Software Skills

- Working knowledge: AutoCAD, GIMP, Photoshop, Affinity software and SketchUp.
- Basic knowledge: Illustrator, InDesign, Kdenlive, Premiere Pro, FreeCAD and QGIS.
- Currently learning: Revit, Blender and Python.

Competitions

- Moon Camp Challenge 2018/2019
- Luiz Conceição 2022
- Roca's One Day Design 2023

Short internship at Architecture studio Urbitraço, Covilhã (2026)
Customer service and sales for 2 summers (2023 and 2024) at Pingo Doce



Personal Information:

André Gonçalves Andrade
Covilhã, Castelo Branco, Portugal

Contacts:

andre.andrade@ubi.pt
LinkedIn agandrade
Socials @aga_100kr

Languages:

Native:	Portuguese
B2:	English and Spanish
A1:	Italian and Greek
Beginner:	Coding